


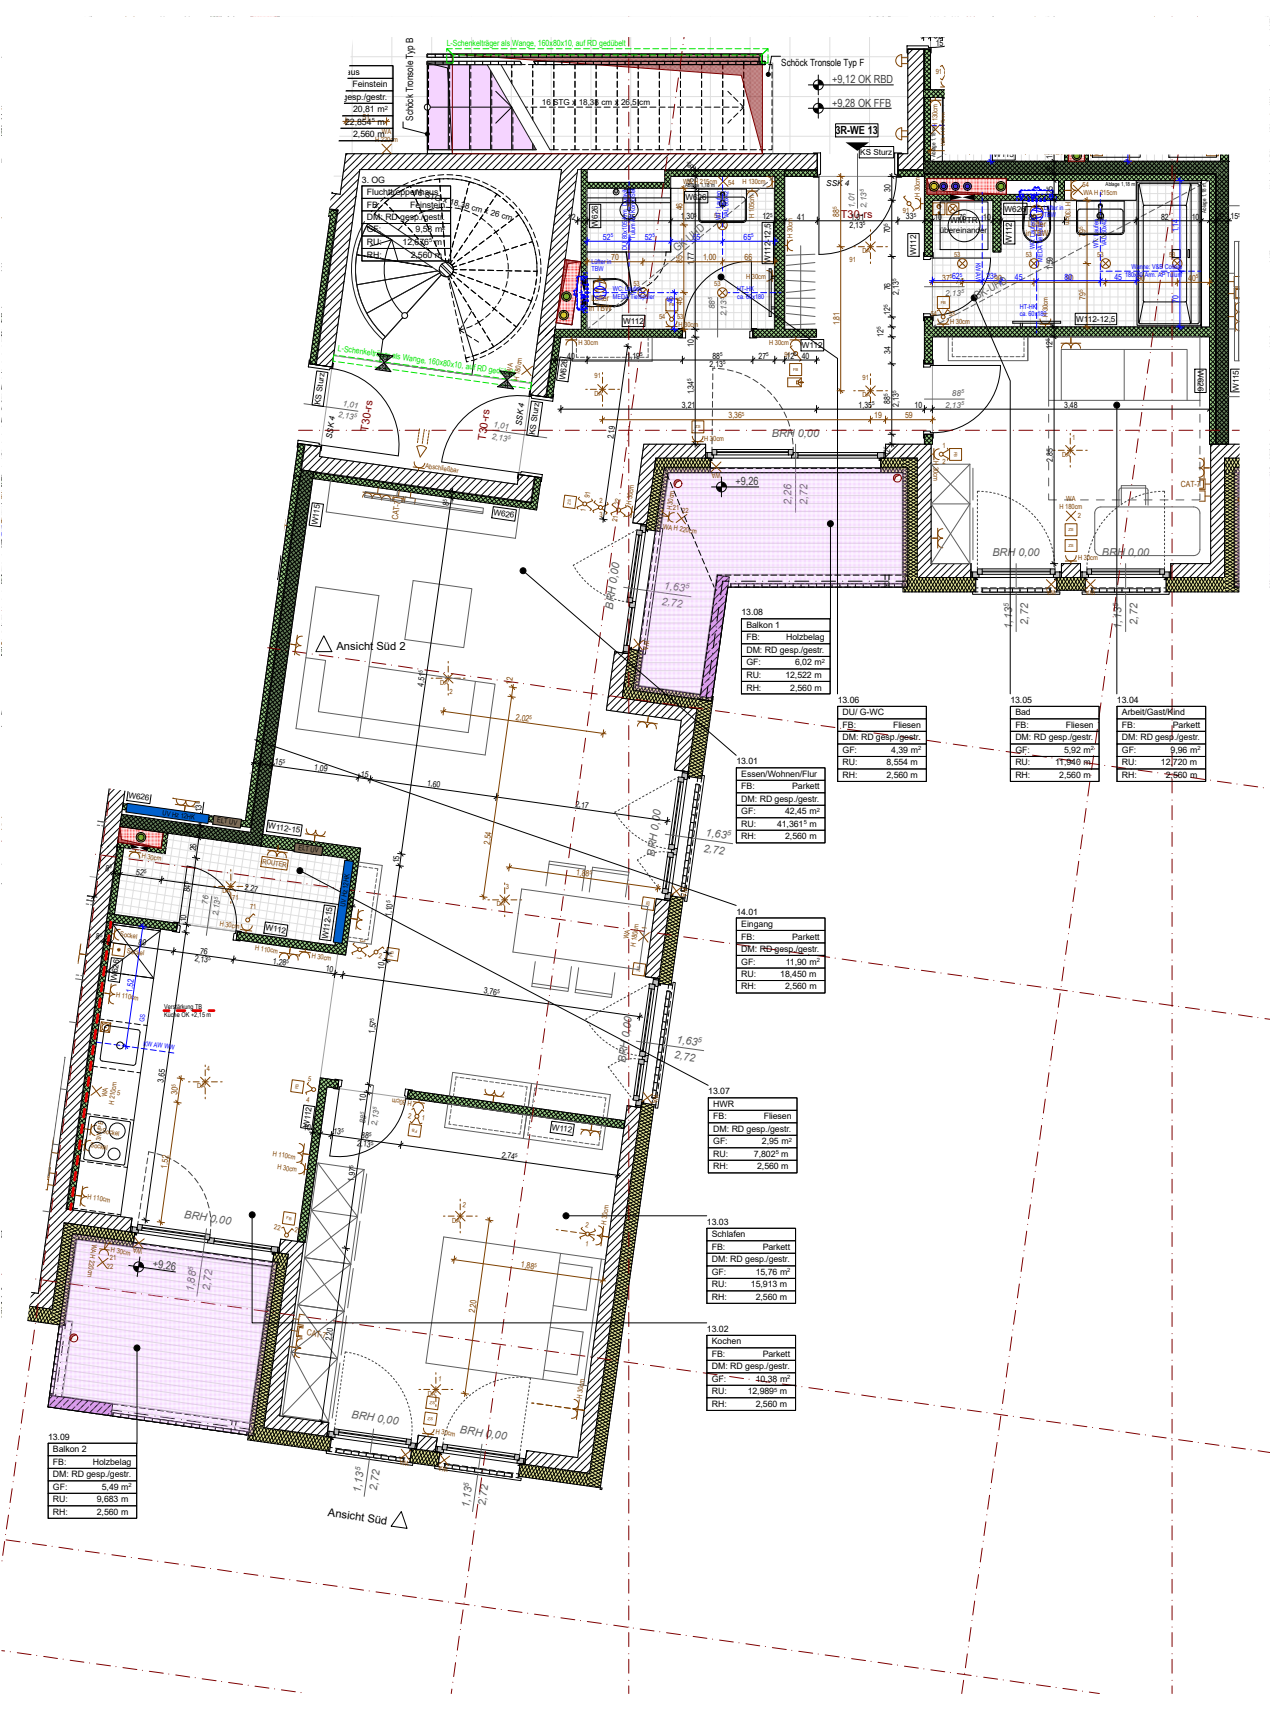

Schöck Transole Typ B
Flächen
20,81 m²
22,854 m²
2,560 m

Schöck Transole Typ F
+9.12 OK RBD
+9.28 OK FFB
BR-WE 13
KS Sturz

OG
Flächen
FB: Parkett
DM: RD gesp./gestr.
GF: 9,34 m²
RU: 12,842 m
RH: 2,560 m

13.08
Balkon 1
FB: Holzbelag
DM: RD gesp./gestr.
GF: 6,02 m²
RU: 12,522 m
RH: 2,560 m

13.06
DU/G-WC
FB: Fliesen
DM: RD gesp./gestr.
GF: 4,38 m²
RU: 8,554 m
RH: 2,560 m

13.05
Bad
FB: Fliesen
DM: RD gesp./gestr.
GF: 5,92 m²
RU: 11,940 m
RH: 2,560 m

13.04
Arbeits/Gast/Wind
FB: Parkett
DM: RD gesp./gestr.
GF: 9,96 m²
RU: 12,720 m
RH: 2,560 m

13.01
Essen/Wohnen/Flur
FB: Parkett
DM: RD gesp./gestr.
GF: 42,45 m²
RU: 41,361 m
RH: 2,560 m

14.01
Eingang
FB: Parkett
DM: RD gesp./gestr.
GF: 11,90 m²
RU: 18,450 m
RH: 2,560 m

13.07
HWR
FB: Fliesen
DM: RD gesp./gestr.
GF: 2,35 m²
RU: 7,802 m
RH: 2,560 m

13.03
Schlafen
FB: Parkett
DM: RD gesp./gestr.
GF: 15,76 m²
RU: 15,913 m
RH: 2,560 m

13.02
Kochen
FB: Parkett
DM: RD gesp./gestr.
GF: 40,38 m²
RU: 12,989 m
RH: 2,560 m

13.09
Balkon 2
FB: Holzbelag
DM: RD gesp./gestr.
GF: 5,49 m²
RU: 9,683 m
RH: 2,560 m

Ansicht Süd